

Planning Commission Staff Report

File # 4S22/SUB-000226-2022

**Consideration of a Preliminary Plat for the
Fields Subdivision Located at 4768 S 1175 W
for Approximately 0.72 Acre**



Department of Community Development

Date:	June 7 th , 2022
Meeting Date:	June 14 th , 2022
Agenda Item:	Consideration of a Preliminary Plat for Fields Subdivision
Subject Property Address:	4768 S 1175 W
Applicant:	Nancy Fields
Applicant Agent:	Nancy Fields
Author:	Karyn Kerdolff
Zoning Designation:	R-1-10
General Plan Designation:	Low Density Residential
Parcel #:	21111020270000
Applicable Ordinances:	13.20, 13.21 and 13.30
Agenda item #:	3

Attachments:

Exhibit A: Vicinity Map
Exhibit B: Subject Property
Exhibit C: General Plan Map
Exhibit D: Zoning Map
Exhibit E: Proposed Preliminary Plat
Exhibit F: Civil Set

Summary:

Nancy Fields is requesting consideration of a Preliminary Plat for the property located at 4768 S 1175 W for approximately 0.72 acre. The applicant is proposing a two-lot subdivision. The applicant received final plat approval in 2017 for this proposed subdivision but did not record the approved plat within the approval timeframe.

The property is zoned R-1-10 with a minimum 10,000 square foot lot size. The proposed plat intends to have two (2) lots varying in size from 10,263 square feet to 21,139 square feet. The proposed subdivision has one lot with an existing single-family home on it and one proposed lot to the south. To meet code requirements, the lot sizes must be at least 80' wide. The minimum home size required is 1,200 square feet for a one-story home or 1,875 for a two-story home. The setbacks for the R-1-10 zone are as follows:

Front Yard	Side Yard	Side Yard Combined	Rear Yard
25 feet	5 feet	16 feet	15 feet

As proposed the subdivision meets the set-back requirements for the R-1-10 zone.

A few modifications/additions will be required for Final Plat approval, these include the following items including compliance with all applicable code requirements:

- An amendment to the original subdivision plat.
- Legal descriptions need to be correct and consistent throughout the plat.
- A Stormwater Agreement is needed
- A bond is needed for improvements in the right of way
- Hydrants, street lights, and drive-ways need to be added to the site plan.
- A Title Report less than 90 days old is submitted.
- A stipulation needs to be added to the plat that parking is not allowed on the shared access easement.

Adjacent Land Uses

North	South	East	West
OS (Open Space)	R-1-15 (Residential One Dwelling Unit per 15,000 square feet)	R-1-10 (Residential One Dwelling Unit per 10,000 square feet)	OS (Open Space)

Public Comment

As of June 9th, 2022 only one call has been received for this application. It was a request for more information about the subdivision.

Analysis

General Compliance with Development Codes - Development Review Committee

The proposed Preliminary Plat is compliant with the statutes in the Taylorsville Land Development Code.

Findings of Fact

1. This application was initiated by Nancy Fields.
2. The property is zoned R-1-10.
3. The applicant is requesting Preliminary Plat approval for a two (2) lot subdivision.
4. The proposed plat meets the size and setback requirements for the R-1-10 zone.
5. There is an existing single-family dwelling unit on the property that will remain intact, an additional single-family dwelling unit is being proposed on the south side of the property.
6. This property was re-zoned from a R-1-15 to a R-1-10 by the Planning Commission on 6/13/17 and the City Council on 7/5/17.

Staff Recommendation

Staff recommends that the Planning Commission approves the Fields Preliminary Plat for a two (2) lot subdivision.

Conditions of Approval

1. The original plat for 4768 S 1175 W is amended.
2. The plat is recorded with Salt Lake County.
3. A Title Report is submitted and matches the property owner.
4. A Stormwater Agreement is needed
5. A bond is needed for improvements in the right of way
6. Hydrants, street lights, and drive-ways need to be added to the site plan.
7. Legal descriptions need to be correct and consistent throughout the plat.
8. A stipulation needs to be added to the plat that parking is not allowed on the shared access easement.
9. The final plat is compliant with all applicable codes and ordinances.
10. The applicant will comply with the requirements of all reviewing agencies.
11. All applicable fees and bonding are paid prior to recording of the plat.


Recommended Motion

I move that we approve File #4S22/SUB-000226-2022 based on the Findings of Fact and Conditions of Approval as stated in the Staff Report.


Reviewed By:

Department Director _____

Zoning Map: 4768 S 1175 W

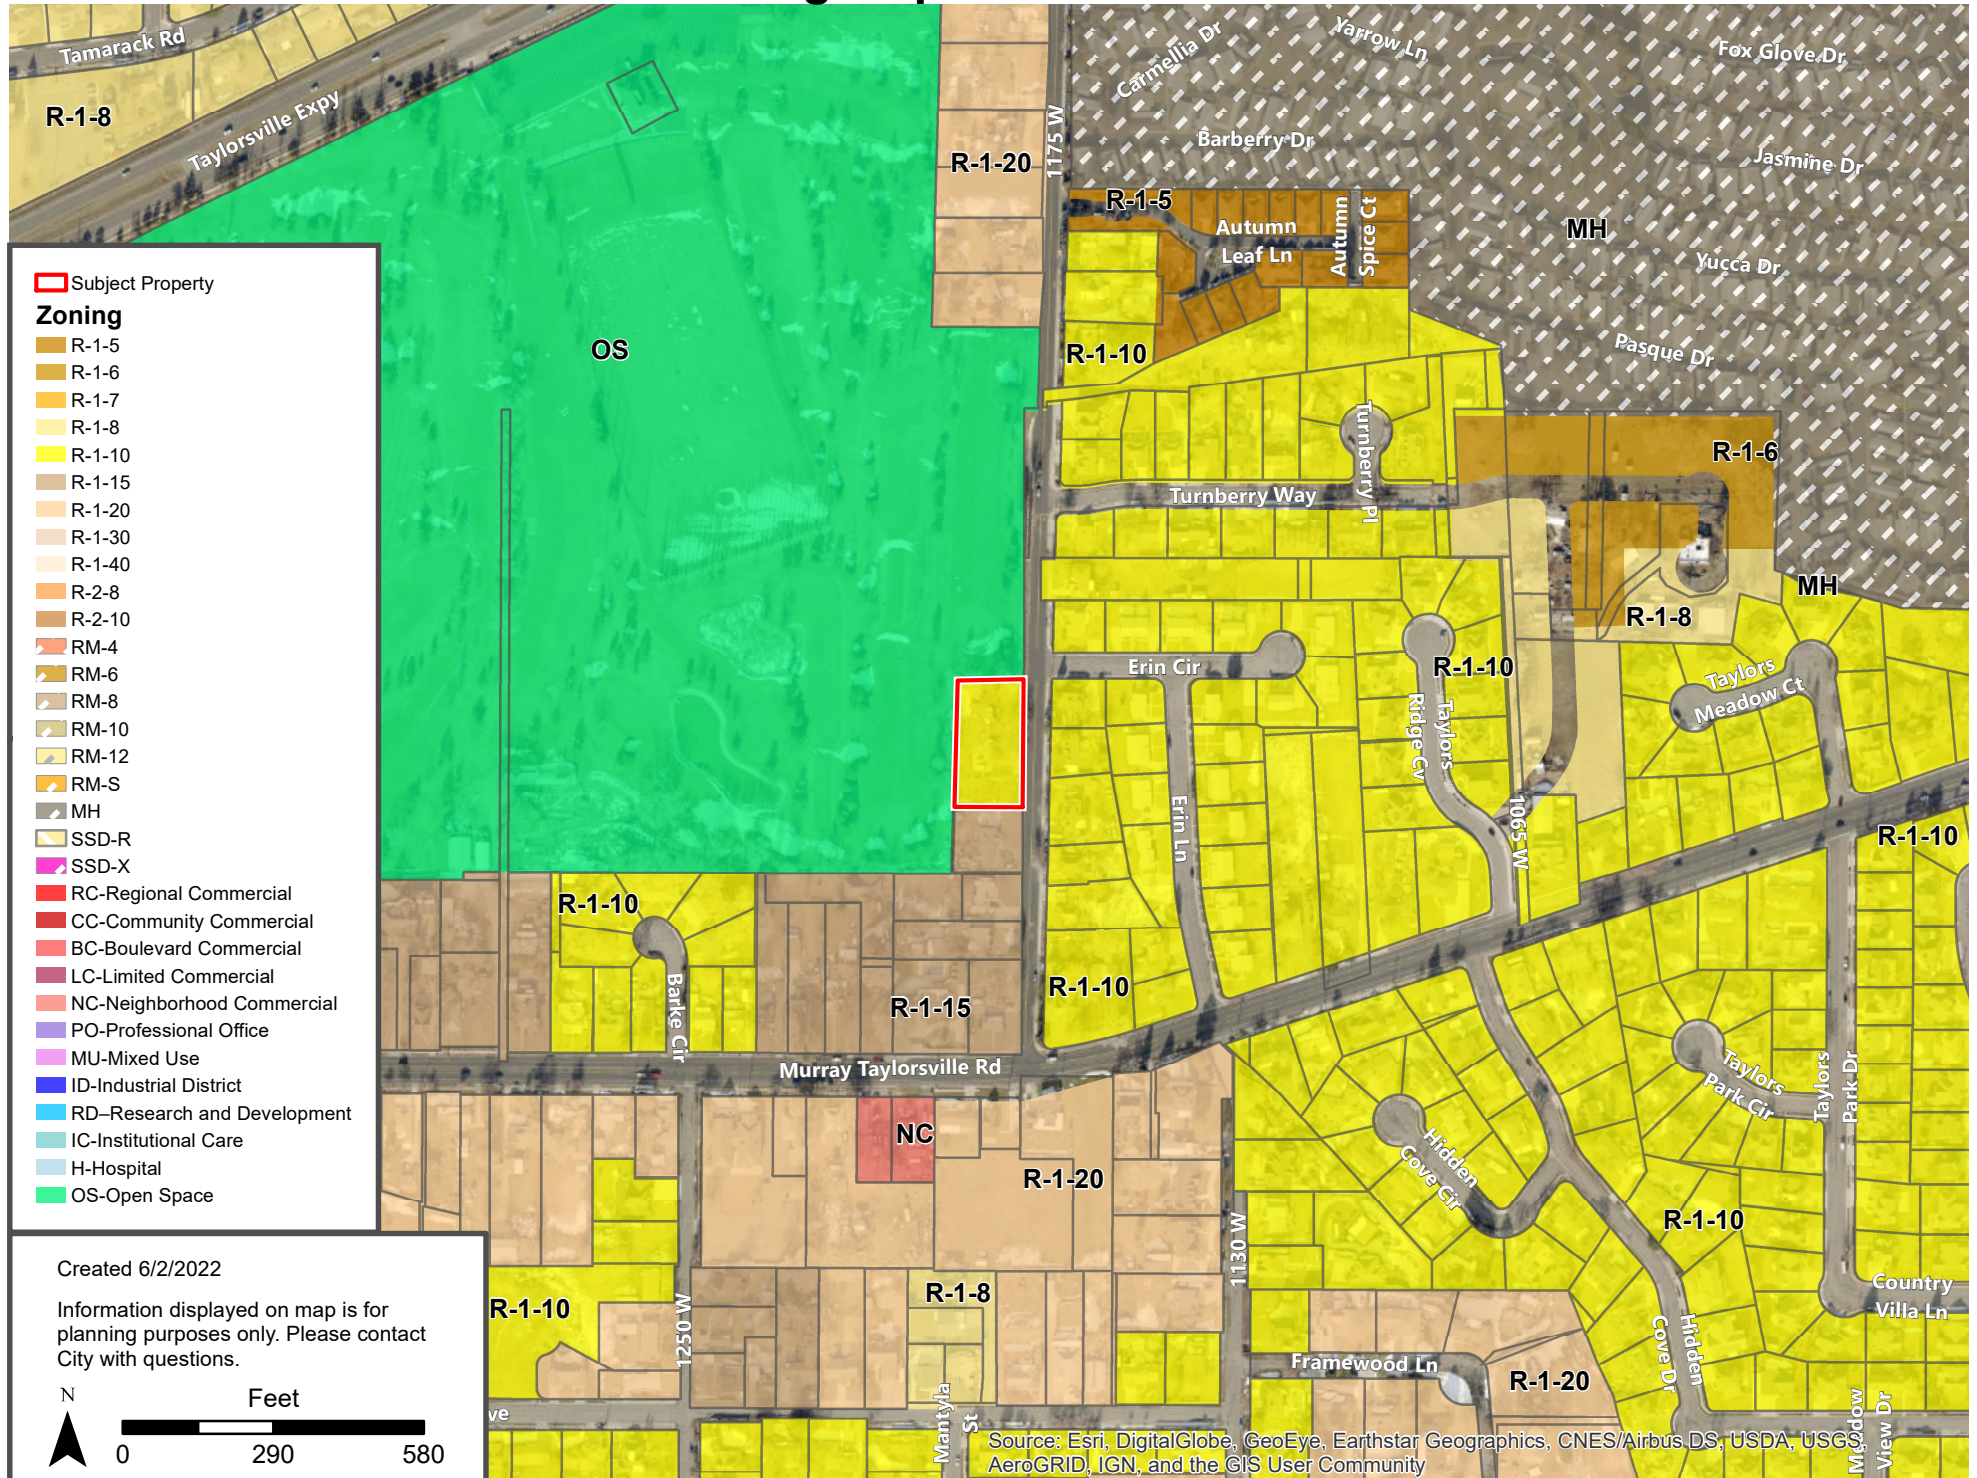

General Plan Map: 4768 S 1175 W

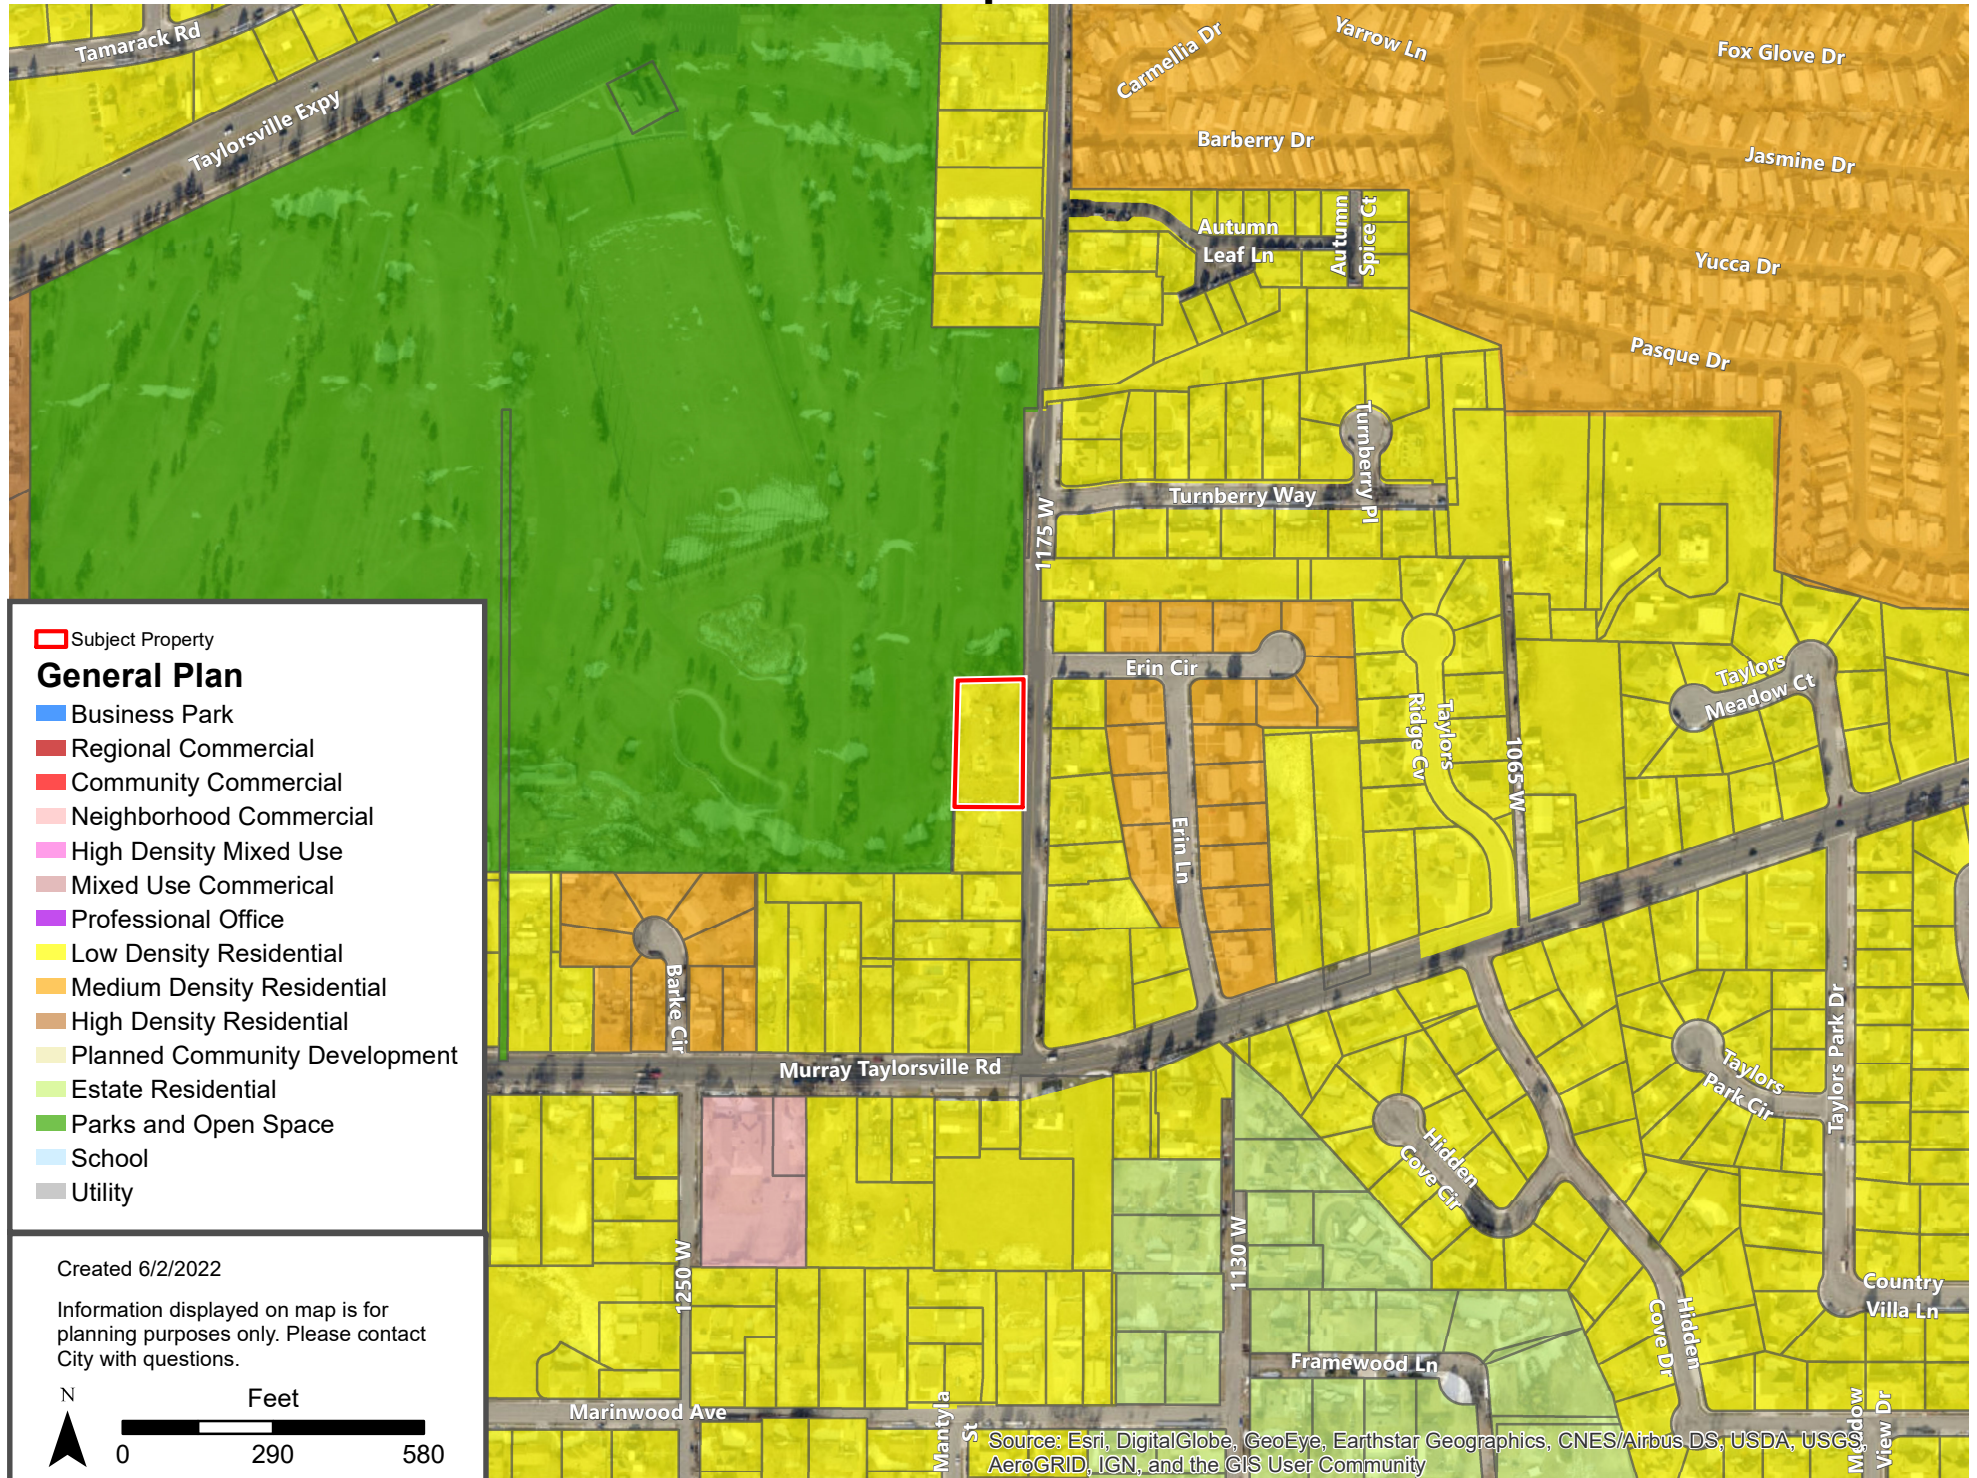


Site Map: 4768 S 1175 W



Vicinity Map: 4768 S 1175 W




THE FIELDS SUBDIVISION

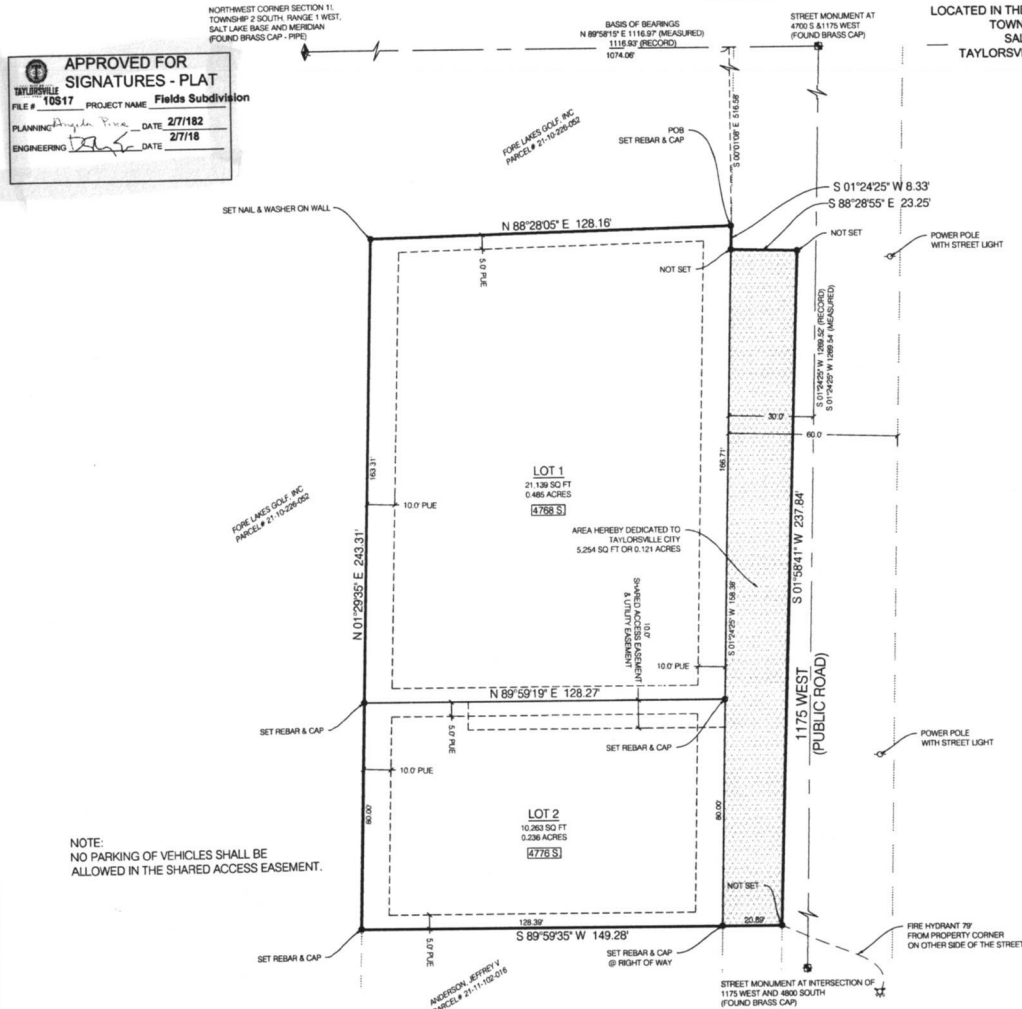

NOTE:
NO PARKING OF VEHICLES SHALL BE
ALLOWED IN THE SHARED ACCESS EASEMENT.

LOCATED IN THE NORTHWEST QUARTER OF SECTION 11,
TOWNSHIP 2 SOUTH, RANGE 1 WEST,
SALT LAKE BASE AND MERIDIAN
TAYLORSVILLE CITY, SALT LAKE COUNTY, UTAH

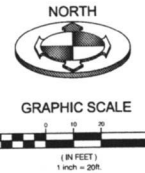

VICINITY MAP

LEGEND

- SECTION CORNER (NOT FOUND)
- S.L.C.D. BRASS CAP MONUMENT (RING & LID)
- BOUNDARY CORNER (SET 1/4 REBAR AND CAP OR AS NOTED ON PLAT)
- EXISTING FIRE HYDRANT
- BOUNDARY LINE
- ADJACENT PROPERTY
- STREET CENTERLINE EXISTING
- EASEMENT
- LOT LINE
- PUBLIC UTILITY EASEMENT AND DRAINAGE EASEMENT

SURVEYOR'S CERTIFICATE

I, BRIAN A. LINAM DO HEREBY CERTIFY THAT I AM A PROFESSIONAL LAND SURVEYOR, AND THAT I HOLD CERTIFICATE NO. 724031 AS PRESCRIBED UNDER THE LAWS OF THE STATE OF UTAH. I FURTHER CERTIFY THAT BY AUTHORITY OF THE OWNERS, I HAVE MADE A SURVEY OF THE TRACT OF LAND SHOWN ON THIS PLAT AND DESCRIBED BELOW, AND HAVE SUBDIVIDED SAID TRACT OF LAND INTO LOTS AND STREETS HEREUPON TO BE KNOWN AS

THE FIELDS SUBDIVISION

AND THAT THE SAME HAS BEEN CORRECTLY SURVEYED AND STAKED ON THE GROUND AS SHOWN ON THIS PLAT.

BOUNDARY DESCRIPTION

BEGINNING AT A POINT ON THE WESTERLY RIGHT OF WAY LINE OF 1175 WEST STREET, SAID POINT BEING NORTH 89°59'19\"/>

CONTAINS 36.657 SQ FT OR 0.842 ACRES
2 LOTS



OWNERS DEDICATION

KNOW ALL MEN BY THESE PRESENTS THAT THE UNDERSIGNED ARE THE OWNERS OF THE ABOVE DESCRIBED TRACT OF LAND, AND HEREBY CAUSE THE SAME TO BE DIVIDED INTO LOTS, TOGETHER WITH EASEMENTS AS SET FORTH TO BE HEREINAFTER KNOWN AS

THE FIELDS SUBDIVISION

AND DO HEREBY DEDICATE FOR THE PERPETUAL USE OF THE PUBLIC ALL ROADS AND OTHER AREAS SHOWN ON THIS PLAT AS INTENDED FOR PUBLIC USE. THE UNDERSIGNED ALSO HEREBY CONVEY TO ANY AND ALL PUBLIC UTILITY COMPANIES A PERPETUAL, NON-EXCLUSIVE EASEMENT OVER THE PUBLIC UTILITY EASEMENTS SHOWN ON THIS PLAT. THE SAME TO BE USED FOR THE INSTALLATION, MAINTENANCE AND OPERATION OF UTILITY LINES AND FACILITIES. THE UNDERSIGNED OWNERS ALSO HEREBY CONVEY ANY OTHER EASEMENTS AS SHOWN ON THIS PLAT TO THE PARTIES INDICATED AND FOR THE PURPOSES SHOWN HEREIN. IN WITNESS WHEREOF, I HAVE HEREUNTO SET HANDS THIS ____ DAY OF _____ A.D. 20__

BY _____
ITS _____

LLC ACKNOWLEDGEMENT

State of Utah }
County of Salt Lake } S.S.
ON THE ____ DAY OF _____, 2018, PERSONALLY APPEARED BEFORE ME _____, WHO AFTER BEING DULY SWORN, ACKNOWLEDGED TO ME THAT HE/SHE IS _____ OF 4768 SOUTH 1175 WEST LLC, A UTAH LIMITED LIABILITY COMPANY, AND THAT THE OWNERS DEDICATION WAS SIGNED BY HIM/HER ON BEHALF OF SAID LLC, AND SAID _____ ACKNOWLEDGED TO ME THAT SAID LLC EXECUTED THE SAME.

MY COMMISSION EXPIRES _____ NOTARY PUBLIC (PRINT NAME)
MY COMMISSION NUMBER _____ NOTARY PUBLIC
RESIDING IN SALT LAKE COUNTY

THE FIELDS SUBDIVISION

LOCATED IN THE NORTHWEST QUARTER OF SECTION 11,
TOWNSHIP 2 SOUTH, RANGE 1 WEST,
SALT LAKE BASE AND MERIDIAN
TAYLORSVILLE CITY, SALT LAKE COUNTY, UTAH

SALT LAKE COUNTY RECORDER


RECORDED # _____
STATE OF UTAH, COUNTY OF SALT LAKE, RECORDED AND FILED AT THE REQUEST OF _____
DATE _____ TIME _____ BOOK _____ PAGE _____
FEE \$ _____
SALT LAKE COUNTY RECORDER

DOMINION ENERGY APPROVED THIS ____ DAY OF _____ A.D. 20__	CENTURYLINK APPROVED THIS ____ DAY OF _____ A.D. 20__	ROCKY MOUNTAIN POWER APPROVED THIS ____ DAY OF _____ A.D. 20__	CITY ENGINEER APPROVED THIS ____ DAY OF _____ A.D. 20__ _____ CITY ENGINEER	BENCHMARK ENGINEERING & LAND SURVEYING 9100 SOUTH STATE STREET SUITE # 100 SANDY, UTAH 84070 (801) 542-7182 WWW.BENCHMARKCIVIL.COM
---	---	--	---	--

TAYLORSVILLE BENNON IMPROVEMENT DISTRICT APPROVED THIS ____ DAY OF _____ A.D. 20__	BOARD OF HEALTH APPROVED THIS ____ DAY OF _____ A.D. 20__ _____ TAYLORSVILLE CITY BOARD OF HEALTH	PLANNING COMMISSION APPROVED THIS ____ DAY OF _____ A.D. 20__ BY THE TAYLORSVILLE PLANNING COMMISSION _____ CHAIRMAN, TAYLORSVILLE PLANNING COMMISSION	APPROVAL AS TO FORM APPROVED AS TO FORM THIS ____ DAY OF _____ A.D. 20__ _____ TAYLORSVILLE CITY ATTORNEY	TAYLORSVILLE COMMUNITY DEVELOPMENT DEPARTMENT I HEREBY CERTIFY THAT THIS OFFICE HAS EXAMINED THIS PLAT AND IT IS CORRECT IN ACCORDANCE WITH INFORMATION ON FILE IN THIS OFFICE. _____ DATE _____ DIRECTOR	CITY OF TAYLORSVILLE MAYOR PRESENTED TO THE MAYOR OF SALT LAKE CITY THIS ____ DAY OF _____ A.D. 20__ AT WHICH TIME THIS SUBDIVISION WAS APPROVED AND ACCEPTED _____ ATTEST _____ RECORDER MAYOR
--	---	---	---	---	---

THE FIELDS SUBDIVISION

LOCATED IN THE NORTHWEST QUARTER OF SECTION 11,
TOWNSHIP 2 SOUTH, RANGE 1 WEST,
SALT LAKE BASE AND MERIDIAN
TAYLORSVILLE CITY, SALT LAKE COUNTY, UTAH

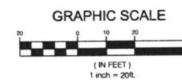


PLAN APPROVAL

TAYLORSVILLE

FILE # 10817 PROJECT NAME Fields Subdivision

PLANNING Angela Price DATE 2/7/18

ENGINEERING [Signature] DATE 2/7/18

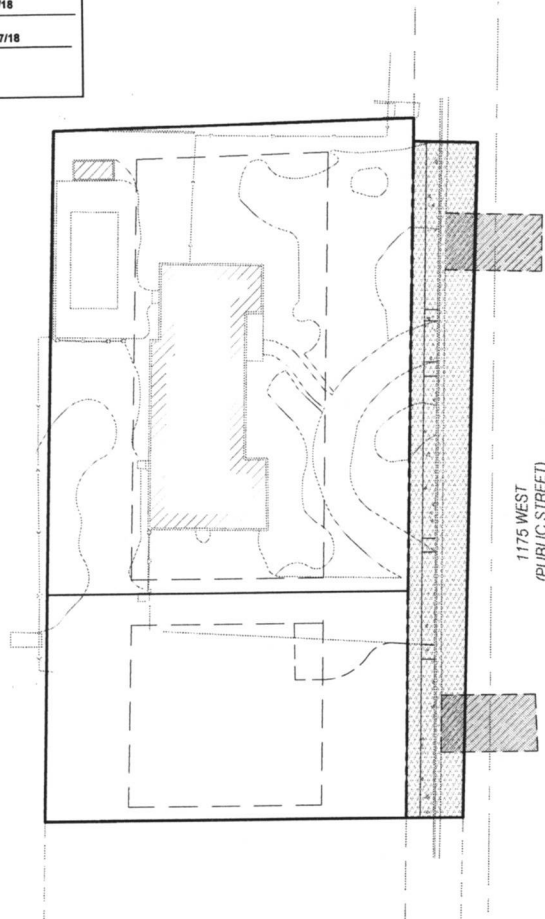

VICINITY MAP
N.T.S.

OWNER/DEVELOPER:
CLARENCE & NANCY FIELDS
4768 SOUTH 1175 WEST
TAYLORSVILLE, UTAH
nfields@metro-now.com

DRAWING INDEX

COVER	COVER SHEET
CGN.01	GENERAL NOTES, LEGEND & ABBREVIATION
CSP.01	SITE PLAN
CUP.01	UTILITY PLAN
CGD.01	GRADING & DRAINAGE PLAN
CEP.01	EROSION CONTROL PLAN
CEP.02	EROSION CONTROL DETAILS
CDT.01	DETAILS & NOTES

CIVIL CONSTRUCTION PLANS

		BENCHMARK ENGINEERING & LAND SURVEYING		PROJECT NO. 1708179	
		9138 SOUTH STATE STREET SUITE # 100 SANDY, UTAH 84070 (801) 542-7192 www.benchmarkcivil.com			
THE FIELDS SUBDIVISION 4768 SOUTH 1175 WEST TAYLORSVILLE, UTAH		DATE 10/10/17	REVISION 1	DATE 10/10/17	COVER 1 OF 8
No. 1 DATE 01/12/18 DESCRIPTION REVISION PER CITY COMMENTS					
No. 2 DATE 02/09/18 DESCRIPTION REVISION PER CITY COMMENTS					

BENCHMARK ENGINEERING CONTACT: DALE K. BENNETT, PLS/PE




PLAN APPROVAL

FILE # 10S17 PROJECT NAME Fields Subdivision

PLANNING _____ DATE 2/7/18

ENGINEERING _____ DATE 2/7/18

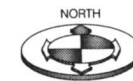

GRAPHIC SCALE



NAME OF T.E.	NL	DATE	DESCRIPTION
ASSTD IN MCP	1	10/17/08	REVISED PER CITY COMMENTS
	2	09/09/08	REVISED PER CITY COMMENTS
DRAWN BY	10/16/2011		
CHECKED BY	17081779dms		
SCALE	0.5"		
			SCALE MEASURES MATCH ON ALL SIZE SHEETS



BENCHMARK
ENGINEERING &
LAND SURVEYING
1718 SOUTH STATE STREET SUITE #100
SANDY, UTAH 84070 (801) 562-7152
www.benchmarkcivil.com

THE FIELDS SUBDIVISION

PROJECT NO. 1708179

SITE PLAN


CSP.01
3 OF 8



**CALL BEFORE YOU DIG.
IT'S FREE & IT'S THE LAW**

BLUE STAKES OF UTAH
UTILITY NOTIFICATION CENTER


1-800-662-4111
www.bluetakes.com

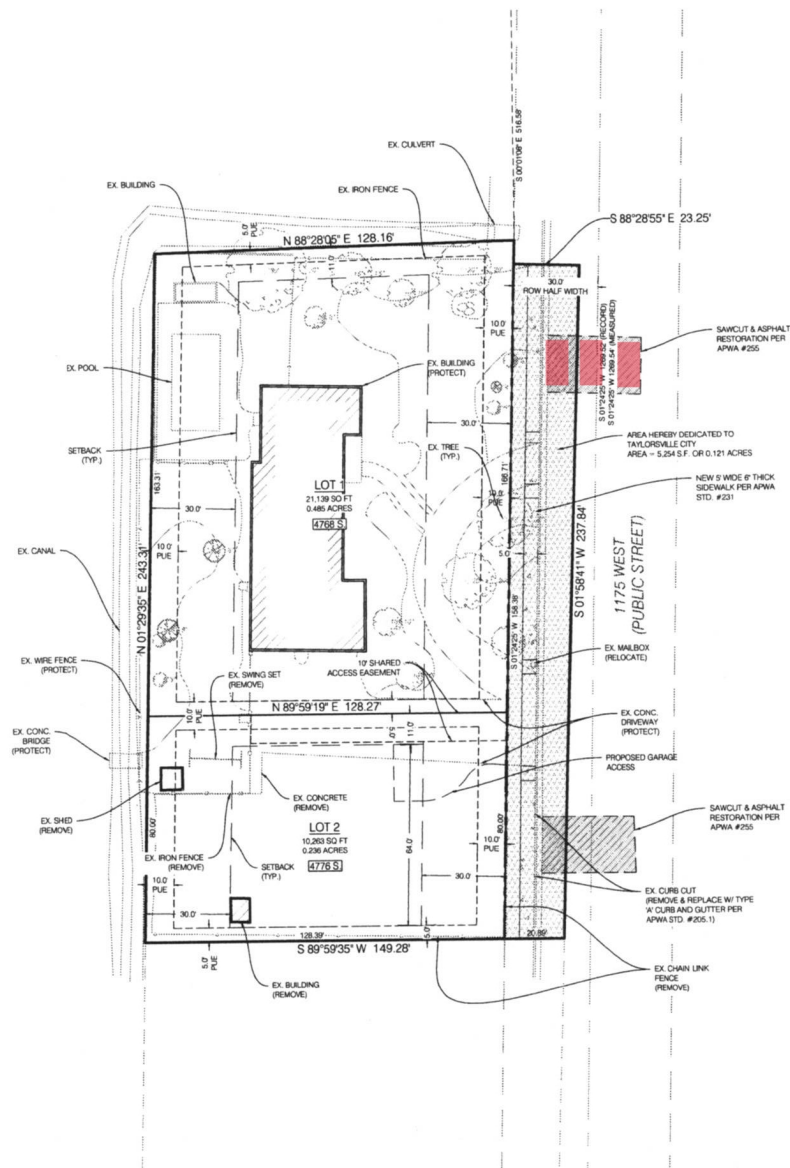

PARTICULARS	S.F.	%
BUILDING	3,528	16.7
HARDSCAPE	5,155	24.4
LANDSCAPE	12,456	58.9
TOTAL	21,139	100

PARTICULARS	S.F.	%
BUILDING	2,000	19.4
HARDSCAPE	1,944	19.0
LANDSCAPE	6,319	61.6
TOTAL	10,263	100

LOT 2 NOTE:
ASSUMED BUILDING FOOTPRINT: 2,000 S.F.
ASSUMED PATIO & DRIVEWAY FOOTPRINT: 500 S.F.

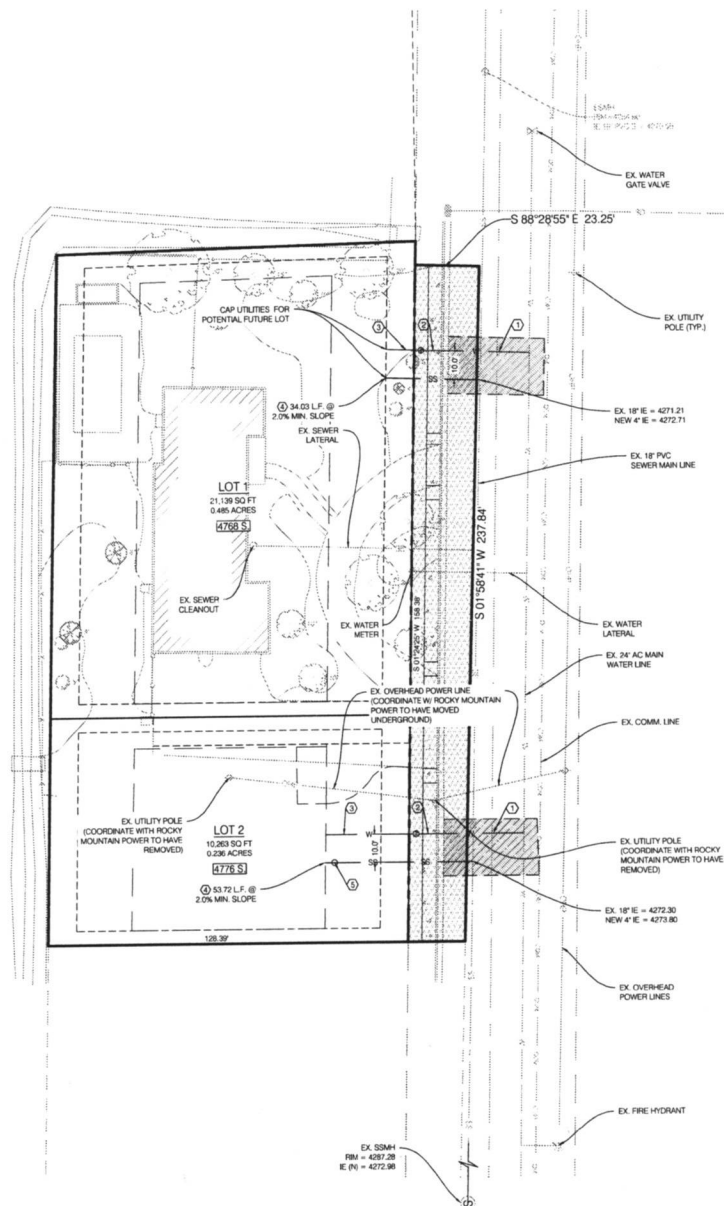

CONSTRUCTION KEY NOTES REFERENCE		
NO.	DESCRIPTION	DETAIL
①	3/4" TYPE K COPPER WATER SERVICE LINE	
②	3/4" WATER METER & VAULT PER APWA #582	2/COT.01
③	3/4" POLY WATER SERVICE LINE	
④	4" PVC SDR-35 SEWER LATERAL PER TBD STD TB-102 & TB-103	1/COT.01
⑤	SEWER CLEANOUT PER TBD STD TB-102	1/COT.01

NOTE:
PRIOR TO FABRICATION OR CONSTRUCTION, BEGIN AT THE LOW END OF ALL GRAVITY UTILITY LINES AND VERIFY THE INVERT ELEVATION OF THE POINT OF CONNECTION AND NOTIFY ENGINEER IF THIS POINT IS HIGHER THAN SHOWN ON THE PLANS FOR A REDESIGN.

NOTE:
POTHOLE TO IDENTIFY ANY CONFLICTS BEFORE ANY PIPE INSTALLATION, CONTACT ENGINEER IF ANY CONFLICTS ARE IDENTIFIED.

CALL BEFORE YOU DIG.
IT'S FREE & IT'S THE LAW.
BLUE STAVES OF UTAH
UTILITY NOTIFICATION CENTER
1-800-962-4111
www.utahstakeout.org

NO.	DATE	BY	DESCRIPTION
1	01/10/2017	CL/JS	REVISIONS
2	01/10/2017	CL/JS	REVISIONS
BENCHMARK ENGINEERING & LAND SURVEYING
1100 S. 1000 E. SUITE 100
SALT LAKE CITY, UT 84143
PHONE: (801) 542-7100
WWW.BENCHMARKUTAH.COM



THE FIELDS SUBDIVISION
4768 SOUTH 11TH ST
TAYLORSVILLE, UT 84143

PROJECT NO. 1708179
UTILITY PLAN
CUP.01
4 OF 8

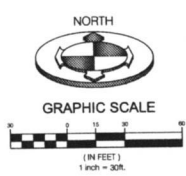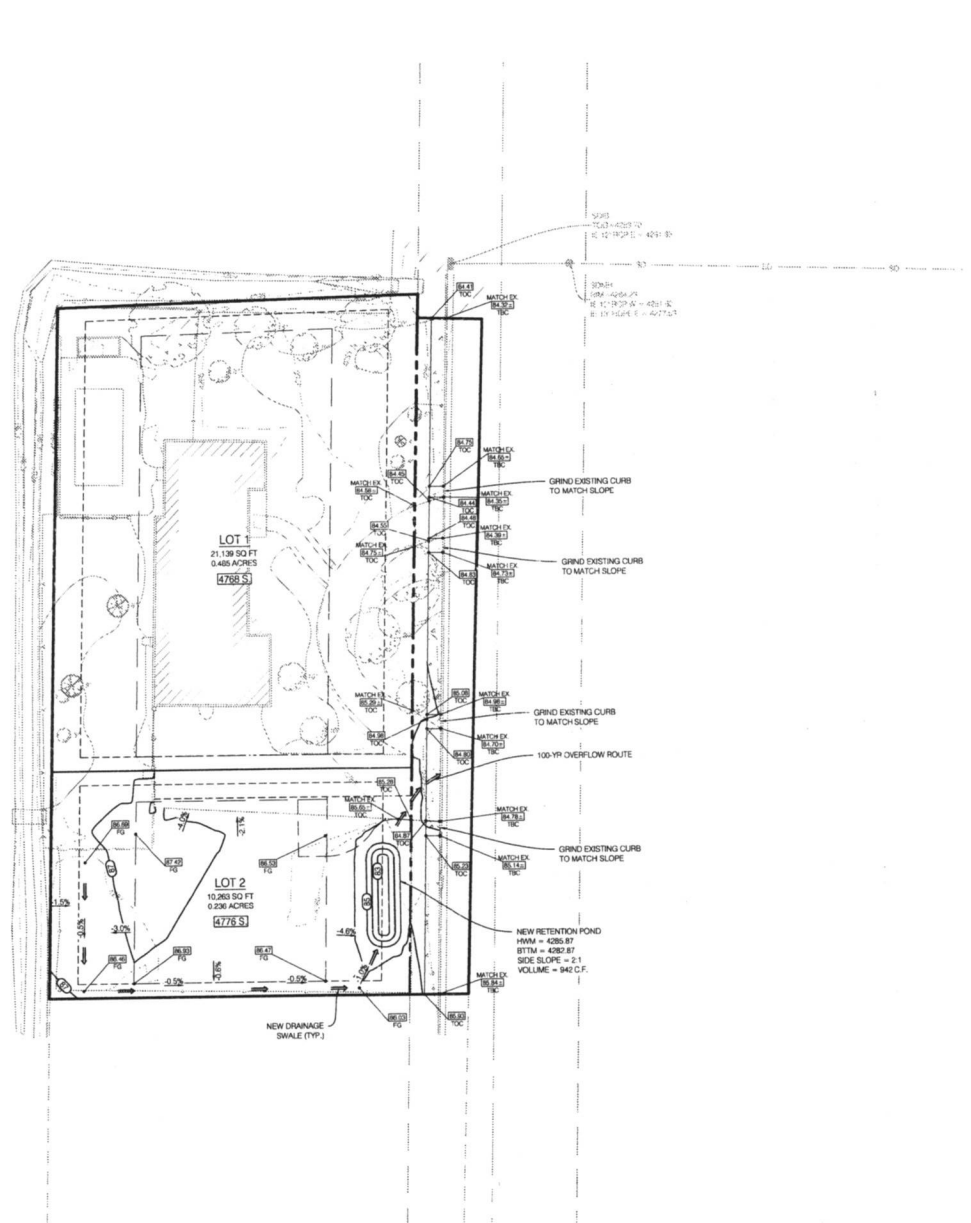

GRADING AND DRAINAGE KEY NOTES REFERENCE		
NO.	DESCRIPTION	DETAIL
①	GRADE SITE TO ELEVATIONS SHOWN ON PLAN	

NOTE:
POTHOLE TO IDENTIFY ANY CONFLICTS BEFORE ANY PIPE INSTALLATION. CONTACT ENGINEER IF ANY CONFLICTS ARE IDENTIFIED.

NOTE:
PRIOR TO FABRICATION OR CONSTRUCTION, BEGIN AT THE LOW END OF ALL GRAVITY UTILITY LINES AND VERIFY THE INVERT ELEVATION OF THE POINT OF CONNECTION AND NOTIFY ENGINEER IF THIS POINT IS HIGHER THAN SHOWN ON THE PLANS FOR A REDESIGN.

STORM DRAINAGE CALCULATIONS					
Rational Method (Q=CIA)					
Area Identification (A)		Rational Coefficient (C)		C*A	
Road =	2,000	0.9		1800 S.F.	
Pavement =	1,942	0.9		1748 S.F.	
Landscaping =	6,521	0.2		1204 S.F.	
Sum:	10,463 S.F.			Sum:	4852 S.F.

NOAA ATLAS 14 (100 YEAR STORM)					
Time (min)	Intensity (in/hr)	Rainfall (in/hr)	Excess (in/hr)	Allowed Discharge (cfs/ft)	Volume to Detain (cu/ft)
15	4.03	1.908	484	0	484
30	2.71	1.355	543	0	543
60	1.68	1.080	674	0	674
120	0.92	1.814	735	0	735
180	0.82	1.857	745	0	745
360	0.33	1.992	799	0	799
720	0.19	2.316	929	0	929
1440	0.10	2.472	991	0	991

Detention Calculations:
Pond Volume
 Pond 1: Cyl 3D = 942 cf
 Is there adequate storage? Storage Provided = 942 cf
 Req Storage = 929 cf YES

BENCHMARK
NORTHWEST QUARTER OF SECTION 11,
TOWNSHIP 2 SOUTH, RANGE 1 WEST,
SALT LAKE BASE AND MERIDIAN
STREET MONUMENT AT 1175 WEST
ELEVATION: 4284.76'
DATUM: NAVD83 (PER SALT LAKE COUNTY TIE SHEET)

CALL BEFORE YOU DIG.
IT'S FREE & IT'S THE LAW.
BLUE STAKES OF UTAH
UTILITY NOTIFICATION CENTER

1-800-462-4111
www.bluestakes.org

PROJECT NO. 1708179
DATE 10/18/2017
DRAWN BY M. CHERRY
CHECKED BY M. CHERRY
SCALE AS SHOWN ON ALL SHEETS
ADJUST ACCORDING TO PROVIDED TIE SHEETS

PROFESSIONAL ENGINEER
M. CHERRY
REGISTERED PROFESSIONAL ENGINEER
STATE OF UTAH
NO. 10880
EXPIRATION DATE 12/31/2020



BENCHMARK
ENGINEERING &
LAND SURVEYING
10000 FIVE STAR DRIVE
SUITE 100
SALT LAKE CITY, UT 84126
801.462.4111
www.benchmarkutah.com

THE FIELDS SUBDIVISION
4768 SOUTH 11TH WEST
TAYLORSVILLE, UT 84126

1708179

GRADING & DRAINAGE PLAN

CGD.01
5 OF 8

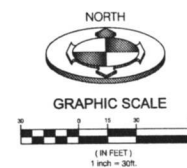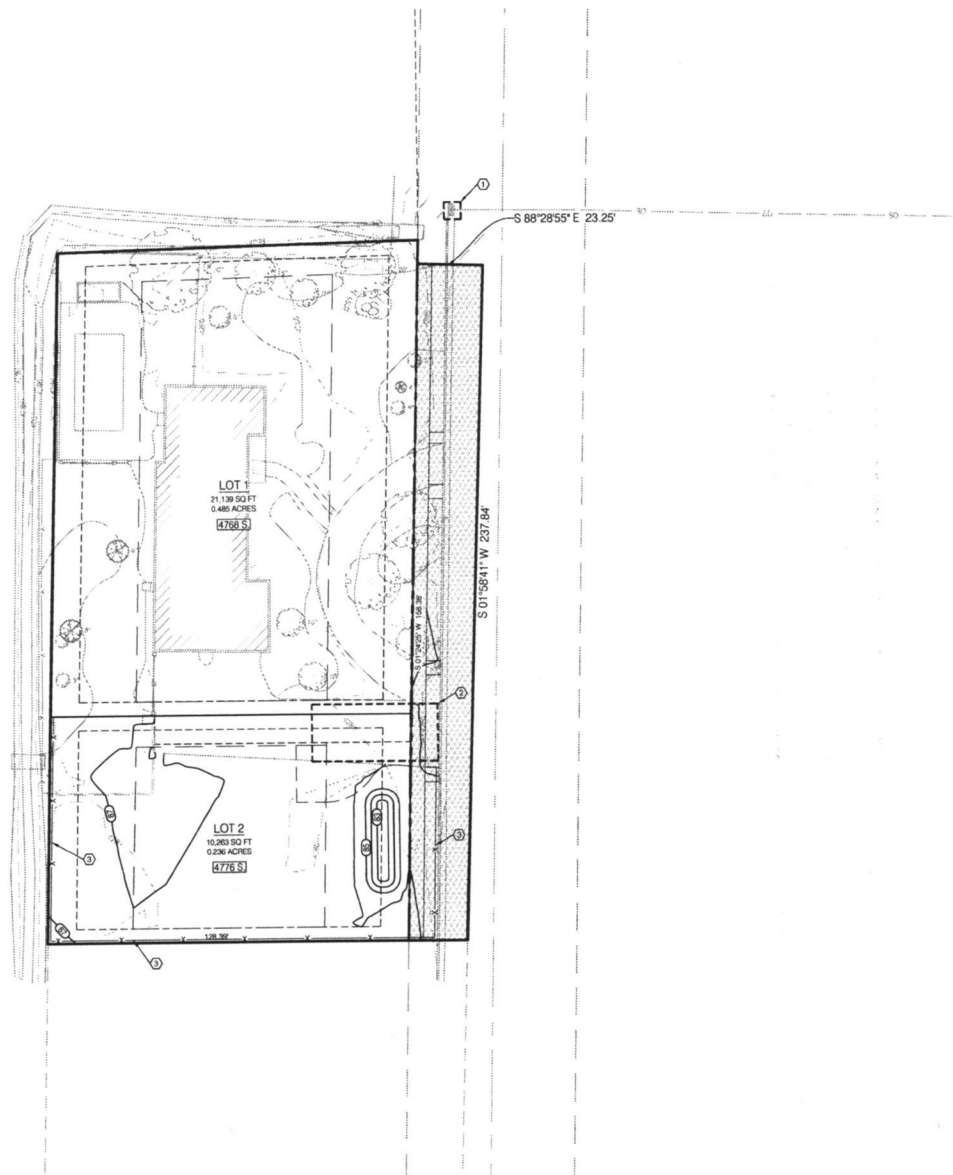

SWPPP KEY NOTES REFERENCE		
PROVIDE, INSTALL AND/OR CONSTRUCT THE FOLLOWING PER THE SPECIFICATIONS GIVEN OR REFERENCED AND THE DETAILS NOTED AND AS SHOWN ON THE CONSTRUCTION DRAWINGS.		
NO.	DESCRIPTION	DETAIL
①	SEDIMENT BARRIER	1/CEP.02
②	TEMPORARY CONSTRUCTION ENTRANCE	2/CEP.02
③	SILT FENCE	3/CEP.02



NO.	DATE	DESCRIPTION
1	10/10/2017	ISSUED FOR CITY COMMENTS
2	10/10/2017	ISSUED FOR CITY COMMENTS
BENCHMARK ENGINEERING & LAND SURVEYING
 15427-182
 SANDY, UTAH 84070
 www.benchmarkutah.com

THE FIELDS SUBDIVISION
 4768 SOUTH 11TH STREET
 TAYLORSVILLE, UT 84143

EROSION CONTROL PLAN
 CEP.01
 6 OF 8

BMP: Inlet Protection - Wattle

IP-W
C:\BMP\IP-W

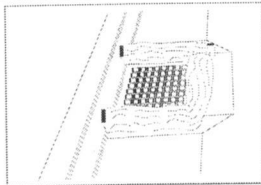

DESCRIPTION:

Sediment barrier erected around storm drain inlet.

APPLICATION:

Construct at storm drainage inlets located down-gradient of areas to be disturbed by construction.

INSTALLATION/APPLICATION CRITERIA:

- Provide up-gradient sediment controls, such as silt fence during construction of inlet.
- When construction of curb and gutter and roadways is complete, install gravel filled wattles around perimeter of inlet.

LIMITATIONS:

- Recommended maximum contributing drainage area of one acre.
- Requires shallow slopes adjacent to inlet.


MAINTENANCE:

- Inspect inlet protection following storm event and at a minimum of once every 14 days.
- Remove accumulated sediment when it reaches 4 inches in depth.
- Look for bypassing or undercutting and repair or realign as needed.

INLET PROTECTION WATTLE

SCALE: NTS

①

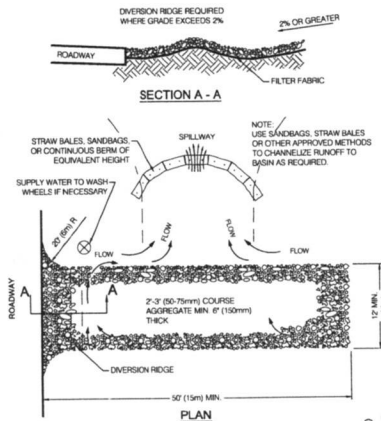


NOTES:

1. THE ENTRANCE SHALL BE MAINTAINED IN A CONDITION THAT WILL PREVENT TRACKING OR FLOWING OF SEDIMENT ONTO PUBLIC RIGHT-OF-WAYS. THIS MAY REQUIRE TOP DRESSING, REPAIR AND/OR CLEAN OUT OF ANY MEASURES USED TO TRAP SEDIMENT.
2. WHEN NECESSARY, WHEELS SHALL BE CLEANED PRIOR TO ENTRANCE ONTO PUBLIC RIGHT-OF-WAY.
3. WHEN WASHING IS REQUIRED, IT SHALL BE DONE ON AN AREA STABILIZED WITH CRUSHED STONE THAT DRAIN INTO AN APPROVED SEDIMENT TRAP OR SEDIMENT BASIN.

TEMPORARY GRAVEL CONSTRUCTION ENTRANCE/EXIT

SCALE: NTS

②

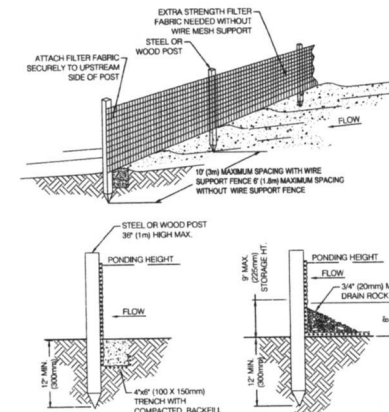

TRENCH DETAIL

NOTES:

1. SILT FENCE SHALL BE PLACED ON SLOPE CONTOURS TO MAXIMIZE PONDING EFFICIENCY.
2. INSPECT AND REPAIR FENCE AFTER EACH STORM EVENT AND REMOVE SEDIMENT WHEN NECESSARY. IF (250mm) MAXIMUM RECOMMENDED STORAGE HEIGHT.
3. REMOVED SEDIMENT SHALL BE DEPOSITED TO AN AREA THAT WILL NOT CONTRIBUTE SEDIMENT OFF-SITE AND CAN BE PERMANENTLY STABILIZED.

INSTALLATION WITHOUT TRENCHING

NOT TO SCALE

REF FROM
NEW JOHN McCALLAN

SILT FENCE

SCALE: NTS

③



NO.	DATE	BY	REVISIONS
1	10/15/18	CL/ZS	REVISIONS
2	10/15/18	CL/ZS	REVISIONS
BENCHMARK ENGINEERING & LAND SURVEYING
BENCHMARK CIVIL
4768 SOUTH 11TH WEST
TAYLORSVILLE, UT 84143
801-462-7100
www.benchmarkcivil.com





THE FIELDS SUBDIVISION
4768 SOUTH 11TH WEST
TAYLORSVILLE, UT 84143



1708179

EROSION CONTROL DETAILS

CEP.02
7 OF 8

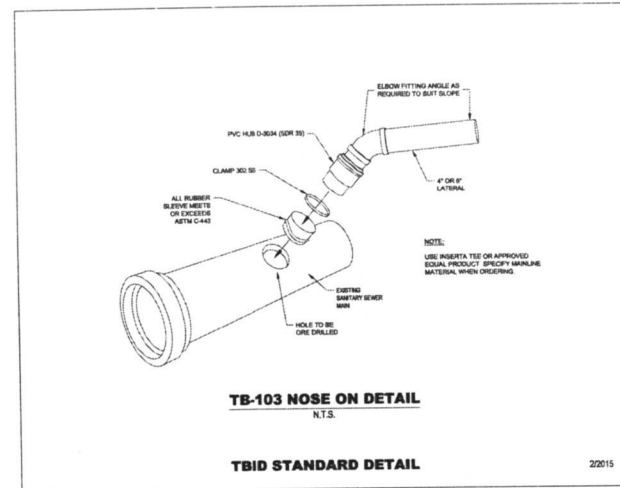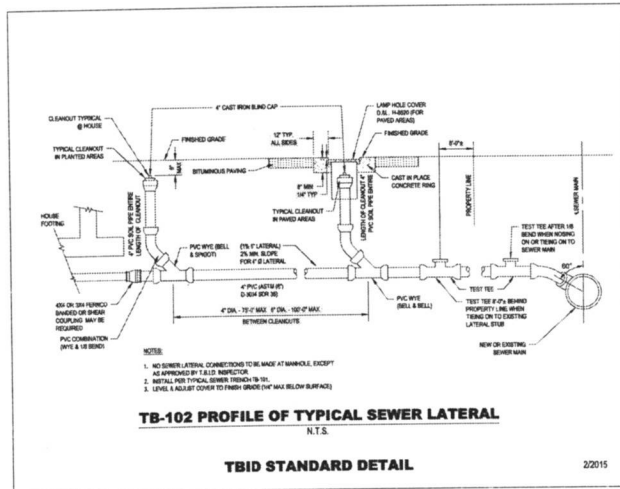

SEWER LATERAL CONNECTION ①
SCALE: NTS

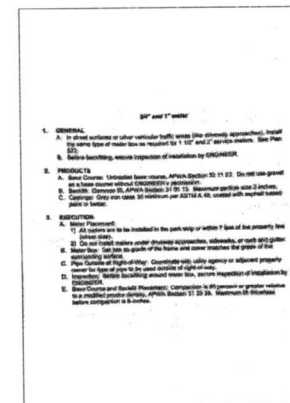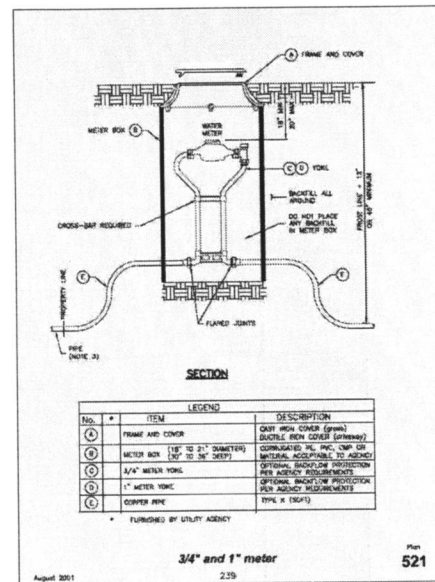

3/4" WATER METER & VAULT DETAIL ②
SCALE: NTS (APWA #521)

NO.	DATE	DESCRIPTION
1	1/1/17	ISSUED FOR CITY COMMENTS
2	1/1/17	ISSUED FOR CITY COMMENTS
BENCHMARK ENGINEERING & LAND SURVEYING
 4768 SOUTH 1ST TAYLORSVILLE, OH 43081
 (614) 291-1700
 www.benchmarkinc.com

THE FIELDS SUBDIVISION
 4768 SOUTH 1ST TAYLORSVILLE, OH 43081
 (614) 291-1700
 www.benchmarkinc.com